I N D I C E

1. OBJETO 2

2. NOMENCLATURA 2

3. NOTAS GENERALES 2

4. LINEAS 3

5. TEXTOS 4

6. CELULAS

-Simbolos de orientación Norte 5
-Simbolos de pilares 6
-Simbolos de base de pilares 7
-Simbolos de escaleras 8
-Simbolos de escalas 9

7. MENU 10

1. OBJETO

Este documento tiene por objeto fijar los detalles de las células a utilizar para la confección de los Planos de Implantación.

Desviaciones a este documento sólo se emplearán en el caso de que sea necesario adaptarse a un contrato o a un cliente determinado.

2. NOMENCLATURA

La nomenclatura de la librería de células para Planos de Implantación es la siguiente: TUBE1Ø4.CEL

3. NOTAS GENERALES

- Las células se obtienen según la representacion que figura en estas hojas. Para distintas orientaciones, utilizar el comando del ángulo activo requerido.

- Los elementos representados en el menú (ver hoja 10), y no cubiertos por las células que aqui se recojen, se construyen mediante comandos del usuario. Estos se activan sobre las casillas correspondientes de dicho menú.

4. LINEAS

Se definen a continuación los distintos espesores de líneas a utilizar en los Planos de Implantación.

TIPO DE LINEA	ESPESOR	LC	WT	UTILIZACION
Línea gruesa	0,6	Ver Nota	5	Límites de bateria
Línea media	0,3	Ver Nota	2	Contorno de equipos
Línea fina	0,2	Ver Nota	1	Resto del dibujo

NOTAS:

1.-El estilo de línea, según los elementos a representar será:

-Línea continua	LC=0	(SOL)
-Línea de trazos	LC=2	(MEDD)
-Línea de ejes (en general)	LC=4	(DOTD)
-Línea de ejes (limites de bateria)	LC=6	(DADD)

2.-Las instalaciones y equipos futuros se representarán con LC=3 (LNGD) manteniendo el WT correspondiente (indicar en el plano "FUTURO").

3.-Las instalaciones y equipos existentes se representarán con LC=2 (MEDD) manteniendo el WT correspondiente (indicar en el plano "EXISTENTE").

5. TEXTOS

Se definen a continuación los atributos de textos a utilizar en los Planos de Implantación.

TEXTO	ESPESOR	WT	TX *
Titulos,límites de area/bateria, códigos de pilares de estructuras.	0,4	3	5
Identificación de equipos	0,3	2	3
Rotulación en general	0,2	1	2,5

* Ver cuadro nº 4 del anexo del PROCEDIMIENTO PARA LA REALIZACION DE PLANOS EN PC (PR-38) para la correspondencia de textos en altura en función de la escala de obtención del plano.

INTECSA UHDE	LIBRERIA DE CELULAS PLANOS DE IMPLANTACION	TUBE104.CEL EDICION 1 HOJA 5 DE

CELULA	CODIGO	AS=	DESCRIPCION
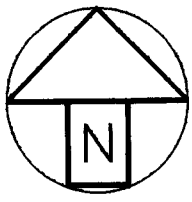	NORTE	SEGUN ESCALA DE OBTENCION DEL PLANO	ORIENTACION PLANOS PLANTA CELULA REPRESENTADA A ESCALA 1:1
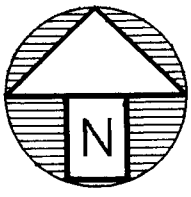	NORTE1		ORIENTACION PLANOS PLANTA CELULA REPRESENTADA A ESCALA 1:1
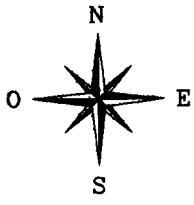	NORTE2		ORIENTACION PLANOS PLANTA CELULA REPRESENTADA A ESCALA 1:2

NOTAS :

TC104005.DGN

INTECSA UHDE	LIBRERIA DE CELULAS PLANOS DE IMPLANTACION	TUBE104.CEL EDICION 1 HOJA 6 DE

CELULA	CODIGO	AS=	DESCRIPCION
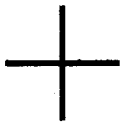	PICR	1,00	PILAR EN CRUZ CELULA REPRESENTADA A ESCALA 1:20
	PIHO	1,00	PILAR H HORIZONTAL CELULA REPRESENTADA A ESCALA 1:20
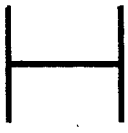	PIVE	1,00	PILAR H VERTICAL CELULA REPRESENTADA A ESCALA 1:20

NOTAS :

TC104006.DGN

INTECSA UHDE	LIBRERIA DE CELULAS PLANOS DE IMPLANTACION	TUBE104.CEL EDICION 1 HOJA 7 DE

CELULA	CODIGO	AS=	DESCRIPCION
	BACI	1,00	BASE CIMENTACION PILAR CELULA REPRESENTADA A ESCALA 1:50
H	BAPH	1,00	BASE PILAR H HORIZONTAL CELULA REPRESENTADA A ESCALA 1:50
I	BAPV	1,00	BASE PILAR H VERTICAL CELULA REPRESENTADA A ESCALA 1:50

NOTAS :

TC104007.DGN

INTECSA UHDE	LIBRERIA DE CELULAS PLANOS DE IMPLANTACION	TUBE104.CEL EDICION 1 HOJA 8 DE

CELULA	CODIGO	AS=	DESCRIPCION
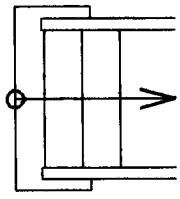	ESC0	1,00	ESCALERA INICIO CON BASE CELULA REPRESENTADA A ESCALA 1:50
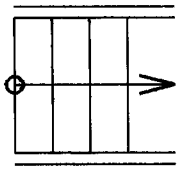	ESC1	1,00	ESCALERA TRAMO INTERMEDIO CELULA REPRESENTADA A ESCALA 1:50
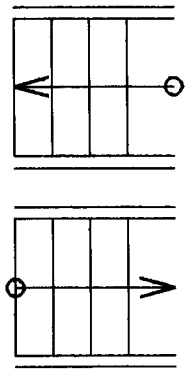	ESC2	1,00	ESCALERA DOS TRAMOS CELULA REPRESENTADA A ESCALA 1:50

NOTAS :

TC104008.DGN

INTECSA UHDE	LIBRERIA DE CELULAS PLANOS DE IMPLANTACION	TUBE104.CEL EDICION 1 HOJA 9 DE

CELULA	CODIGO	AS=	DESCRIPCION
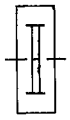	EVCB	1,00	ESCALA VERTICAL CON BASE CELULA REPRESENTADA A ESCALA 1:50
	EVSQ	1,00	ESCALA VERTICAL SIN QUITAMIEDOS CELULA REPRESENTADA A ESCALA 1:50
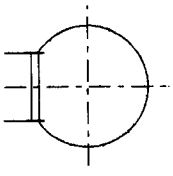	EVSS	1,00	ESCALA VERTICAL CELULA REPRESENTADA A ESCALA 1:50
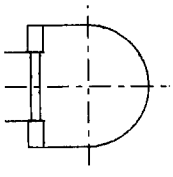	EVSF	1,00	ESCALA VERTICAL SALIDA FRONTAL CELULA REPRESENTADA A ESCALA 1:50
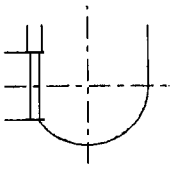	EVSD	1,00	ESCALA VERTICAL SALIDA DERECHA CELULA REPRESENTADA A ESCALA 1:50
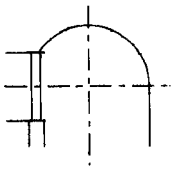	EVSI	1,00	ESCALA VERTICAL SALIDA IZQUIERDA CELULA REPRESENTADA A ESCALA 1:50

NOTAS :

TC104009.DGN
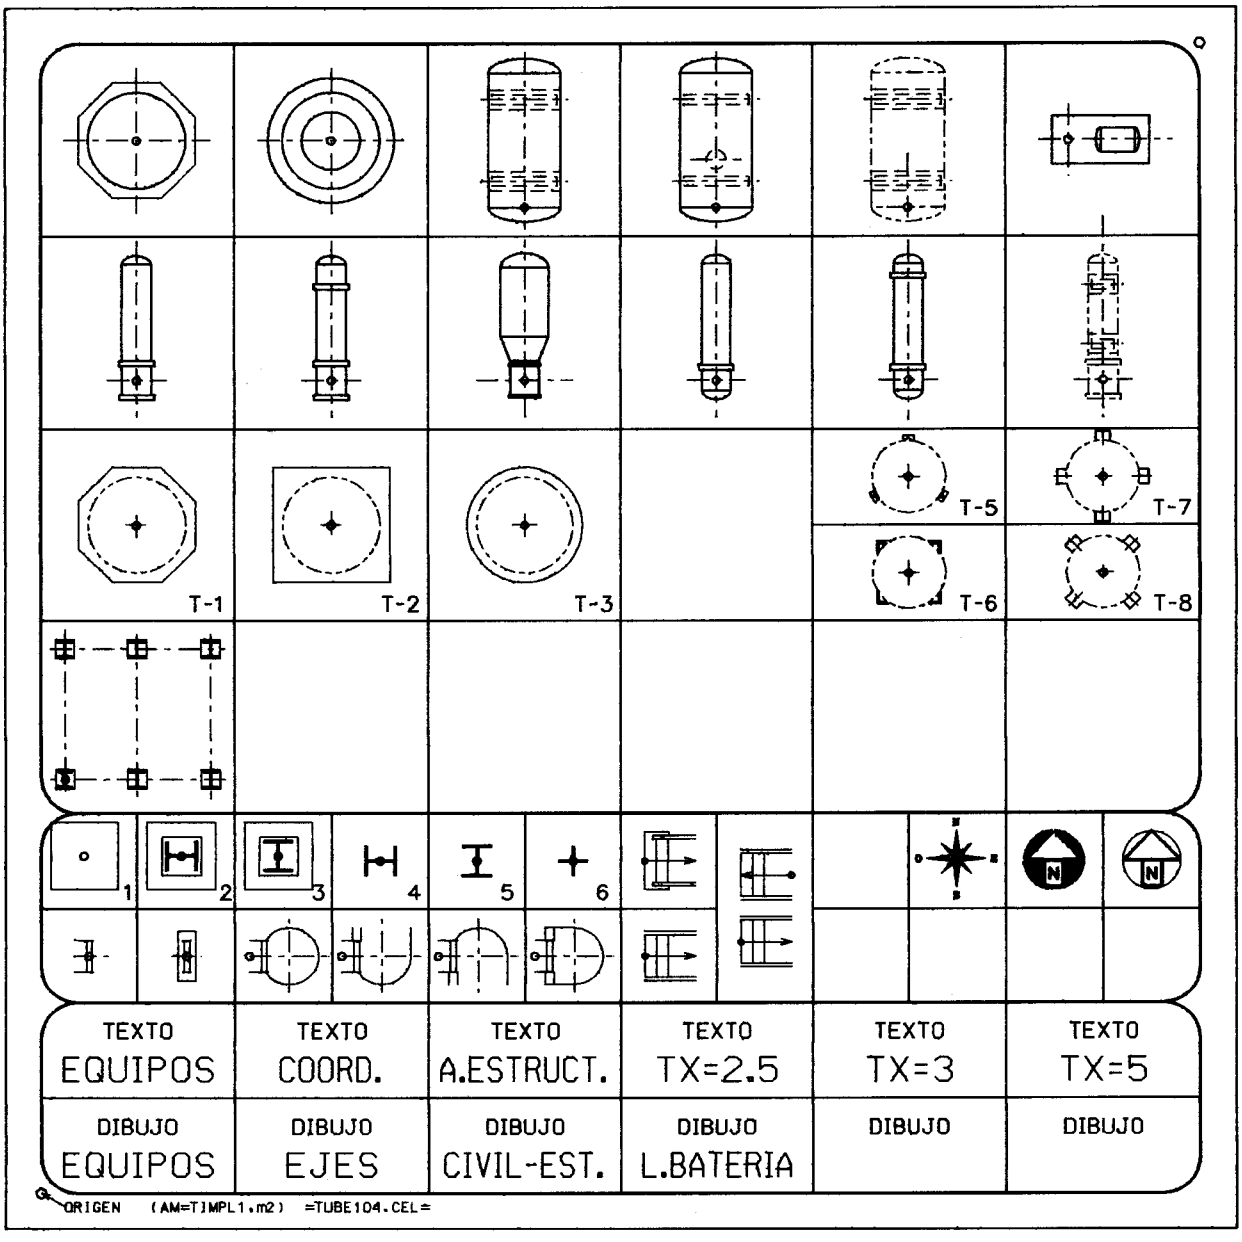
MENU PLANOS DE IMPLANTACION